


[3] Project Architecture

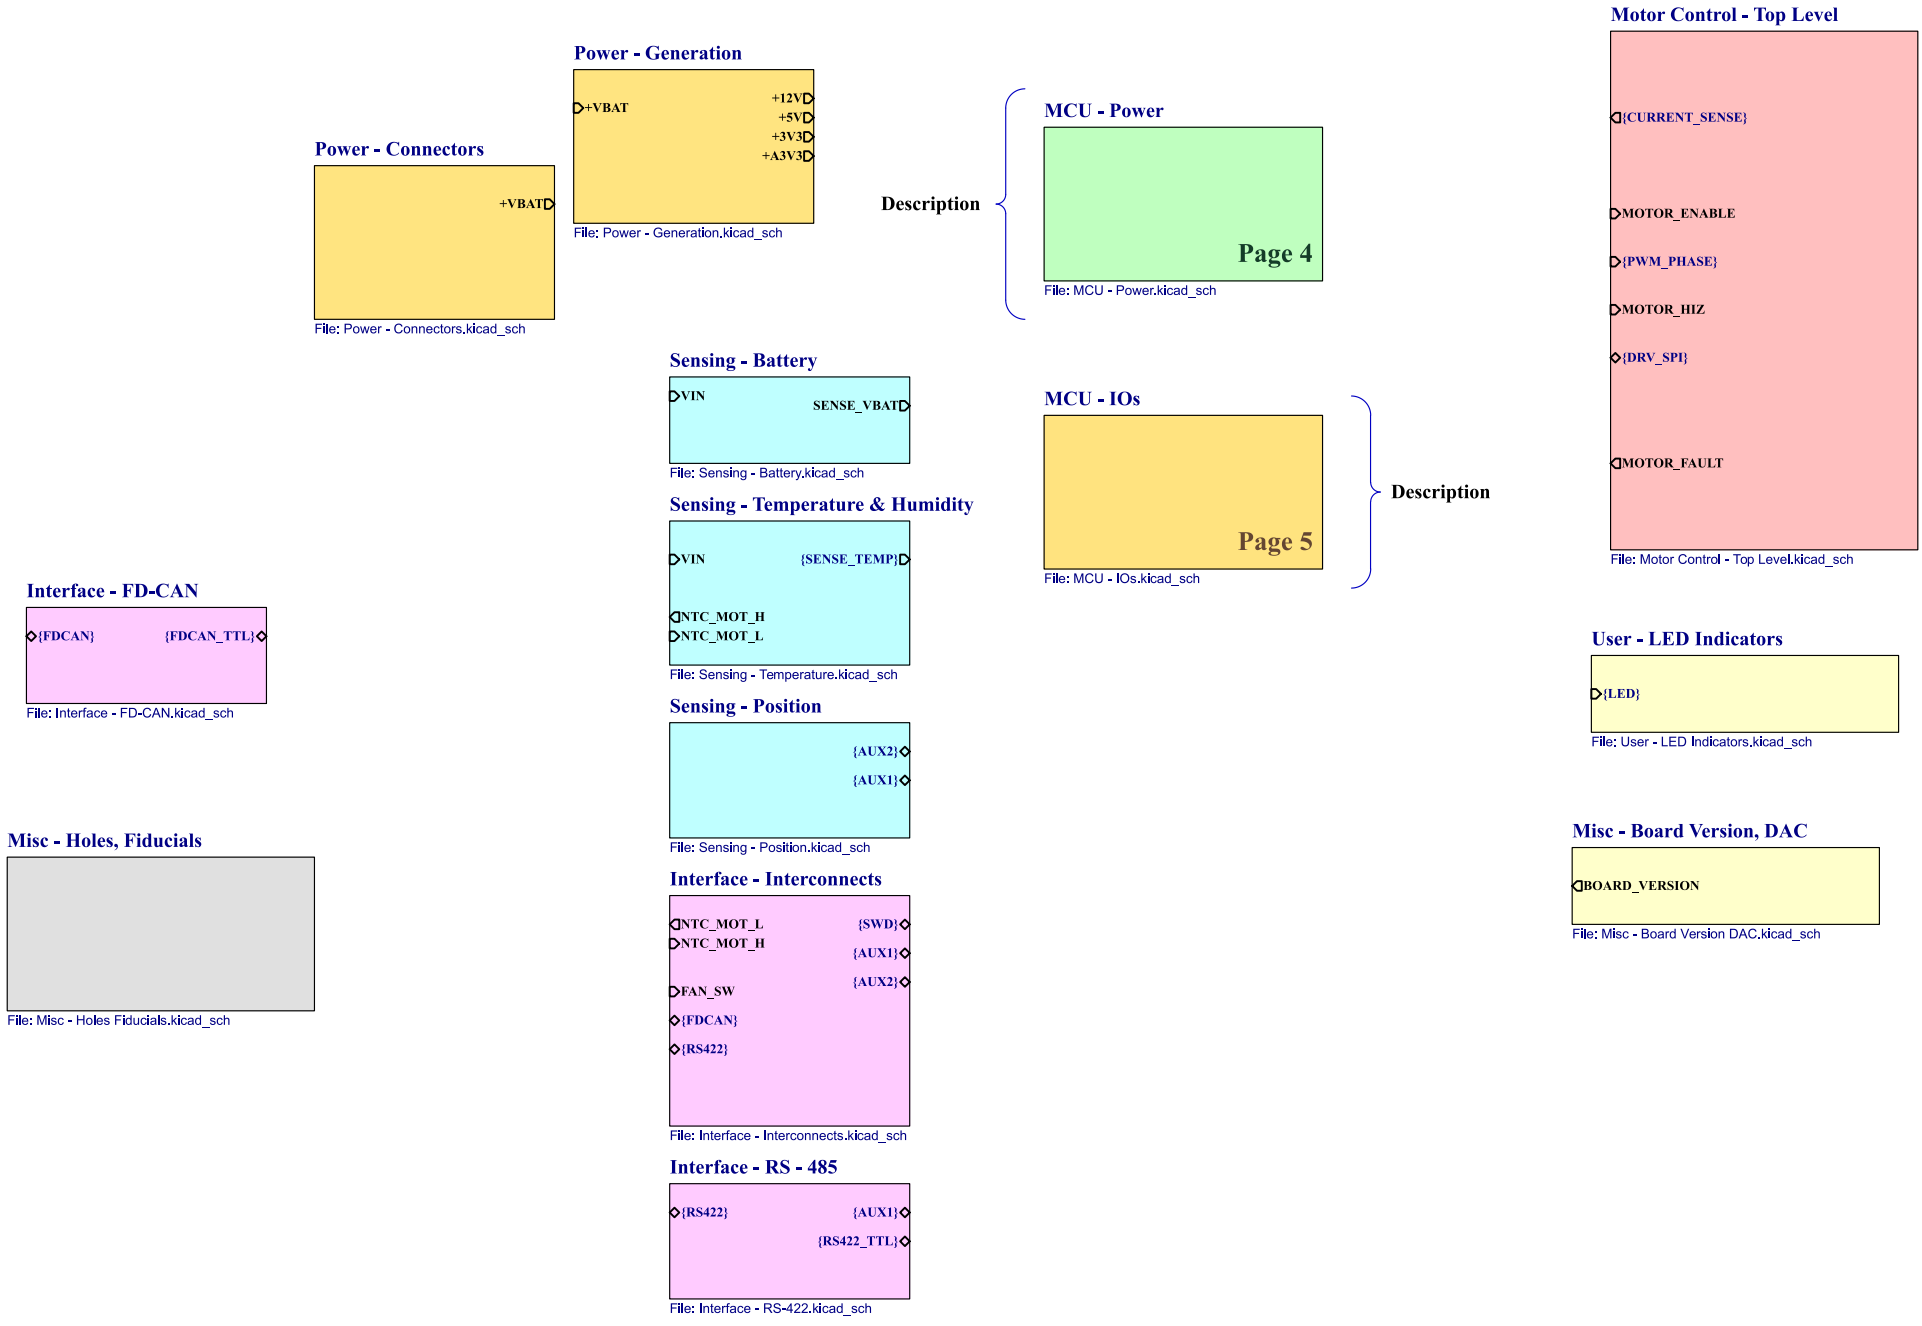

Comments:	Company: Willas		Variant: DRAFT	Git Hash: c12dc26
	Board Name: Motor Control Board		Project Name: Master Hand	
Sheet Title: Project Architecture	File Name: Project Architecture.kicad_sch	Designer: Damon	Date: 2026-06-27	Revision: + (Unreleased)
Sheet Path: /Project Architecture/		Reviewer:	Size: A3	Sheet: 3 of 25