


[3] Project Architecture

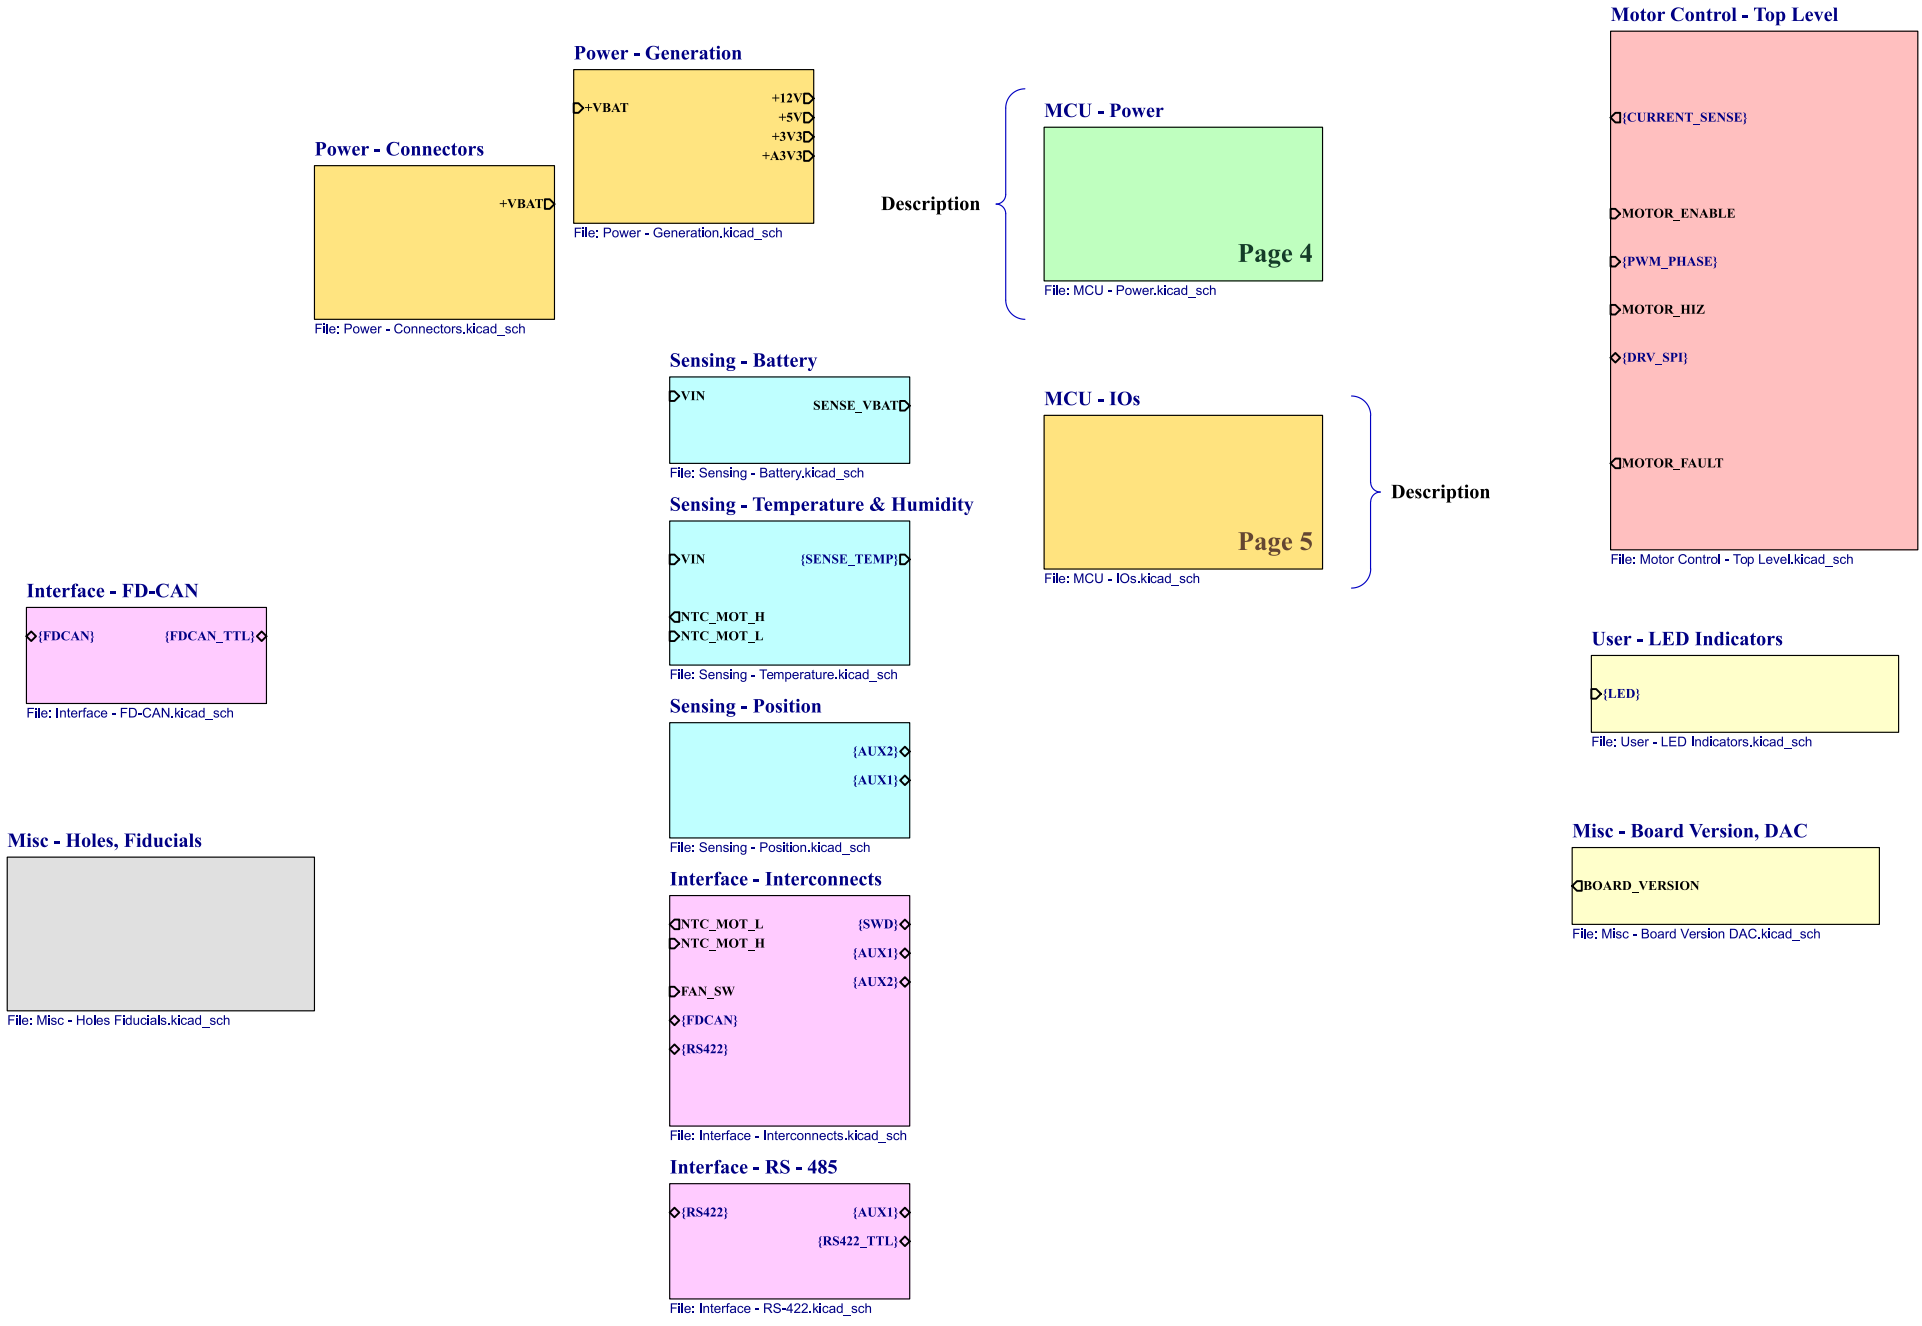

Comments:	Company: WILLAS 		Variant:	Git Hash:
	Board Name: MOTOR CONTROL BOARD		Project Name: MASTER HAND	
Sheet Title: Project Architecture	File Name: Project Architecture.kicad_sch	Designer: DAMON	Date: 2026-06-27	Revision:
Sheet Path: /Project Architecture/		Reviewer:	Size: A3	Sheet: 3 of 25