


[3] Project Architecture

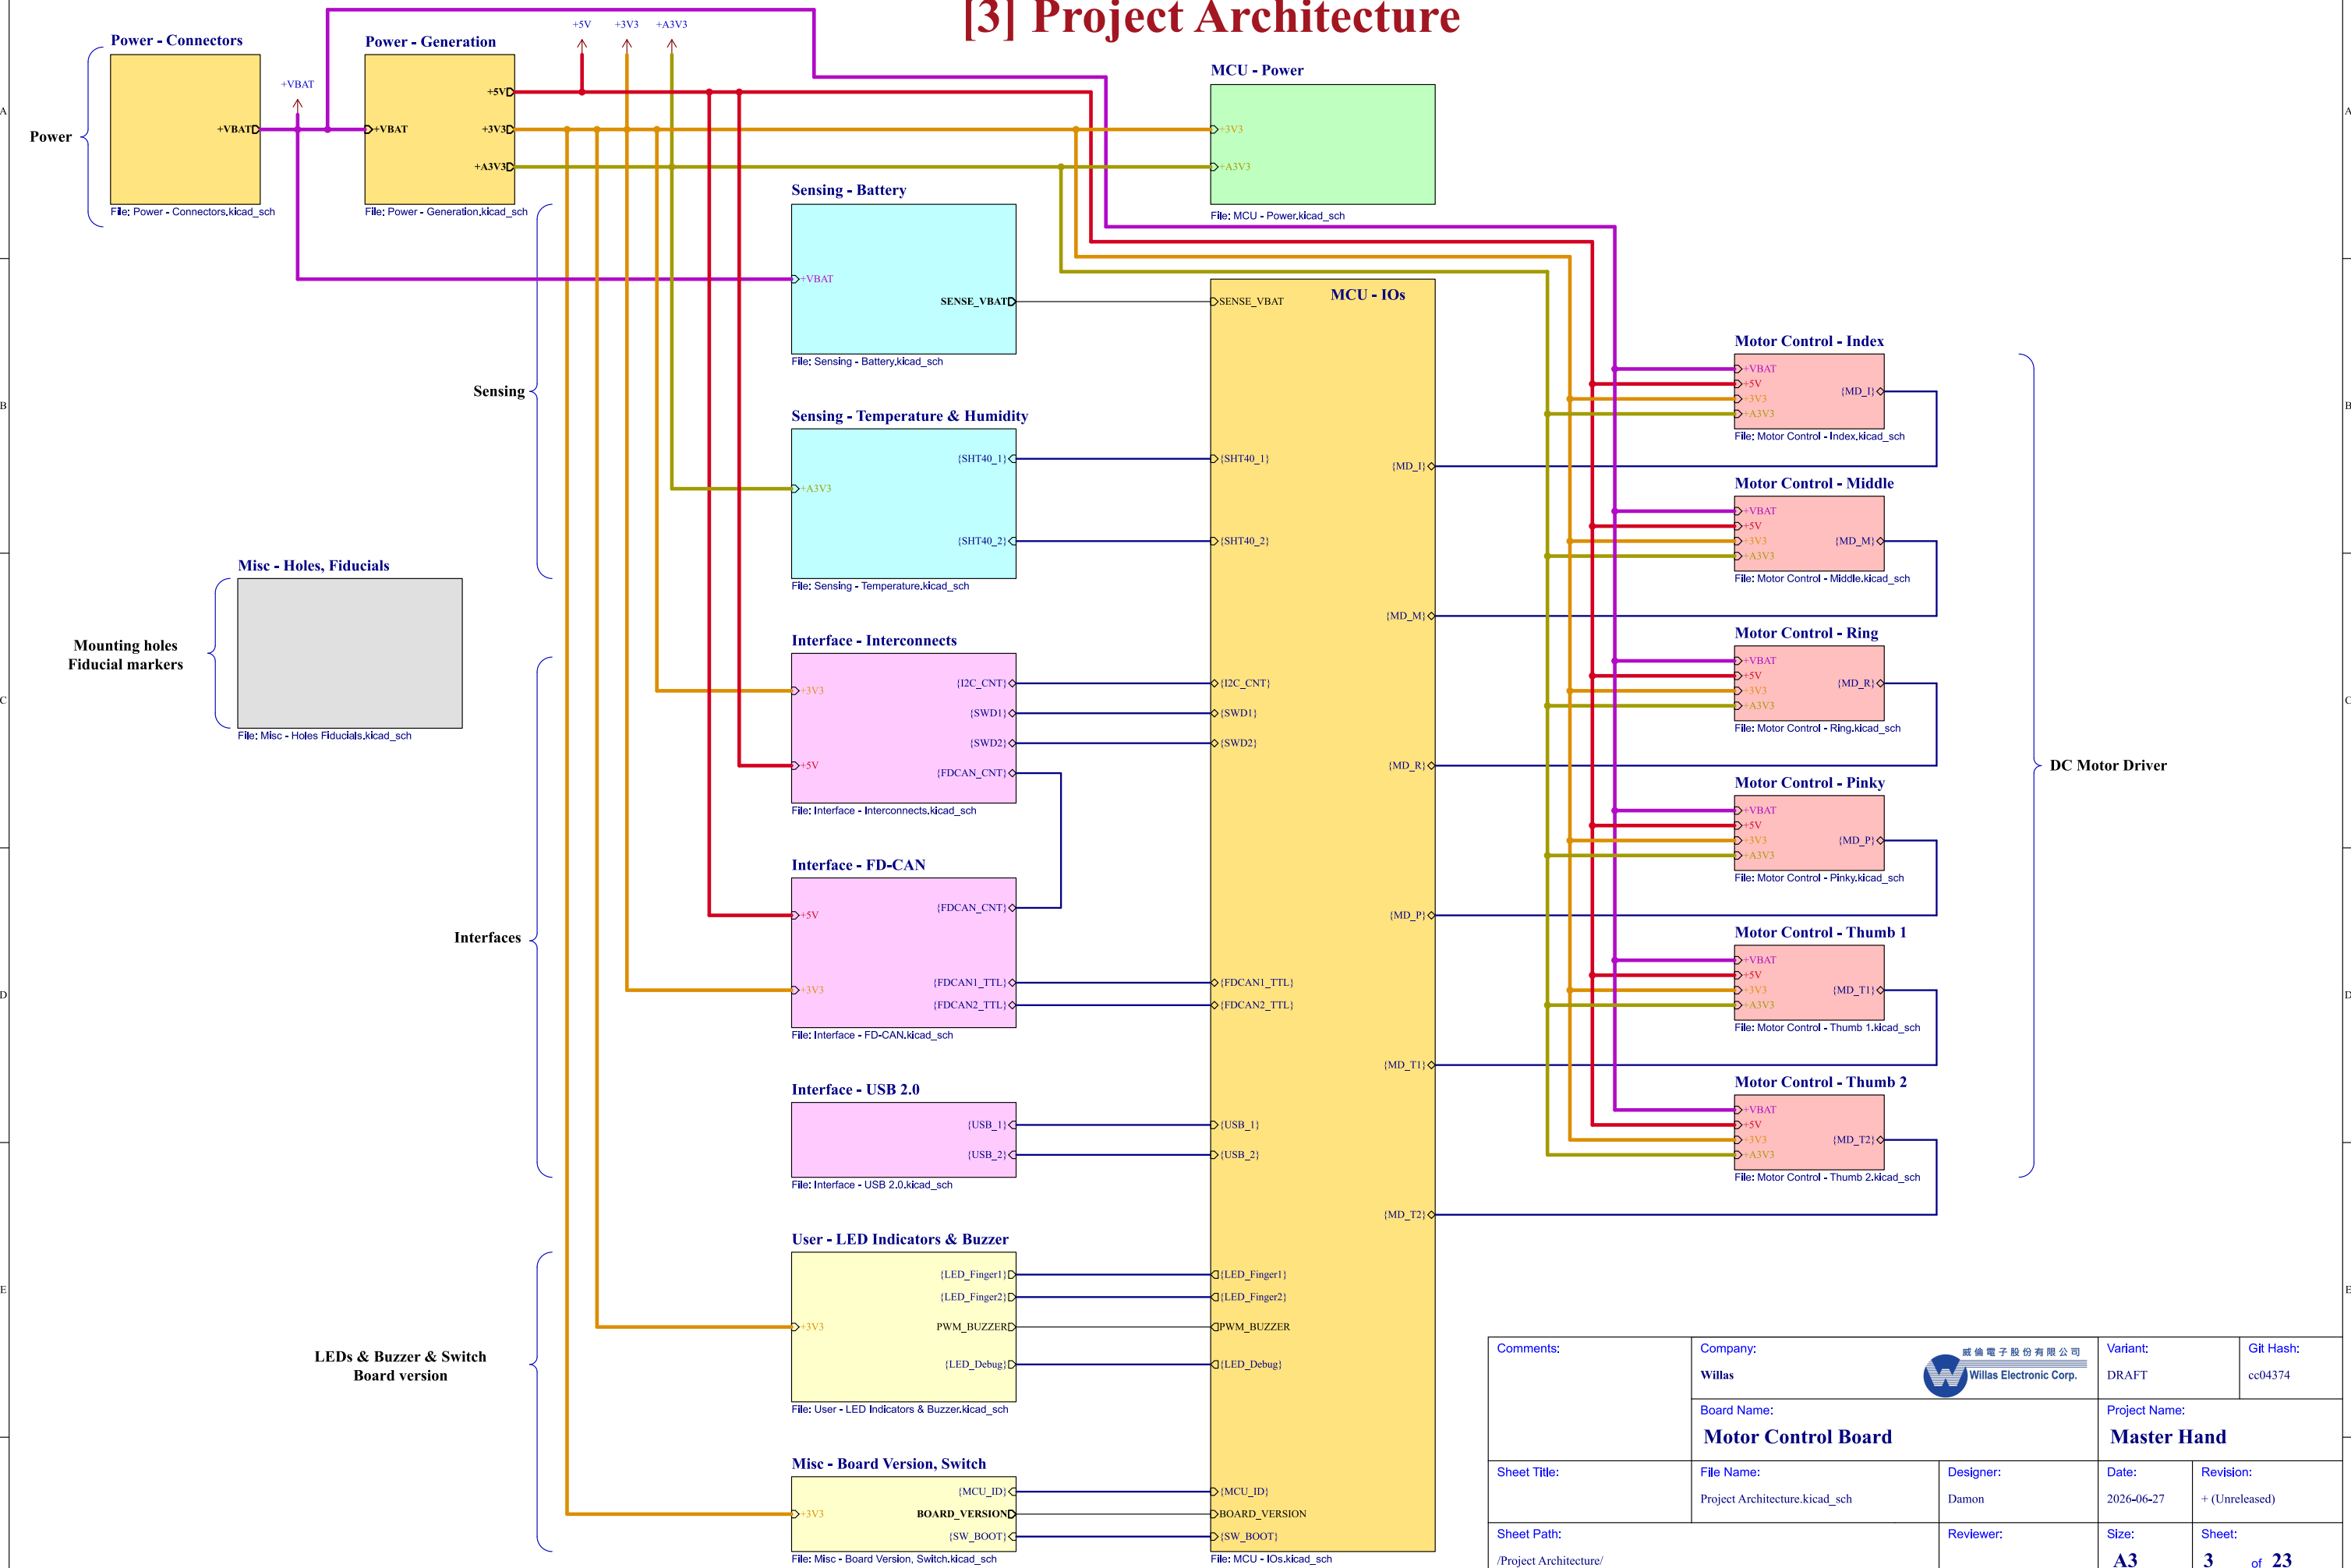

Comments:	Company: Willas 		Variant: DRAFT	Git Hash: cc04374
	Board Name: Motor Control Board		Project Name: Master Hand	
Sheet Title:	File Name: Project Architecture.kicad_sch	Designer: Damon	Date: 2026-06-27	Revision: + (Unreleased)
Sheet Path: /Project Architecture/	Reviewer:	Size: A3	Sheet: 3 of 23	